Propriété dite : Jawharat Al Bahr 16

Située à : Province de Ben Slimane, Commune Mansouria, Lotissement Jawharat Al Bahr.

Titre : 36089/25

Echelle : 1/500

Plan levé en Juillet 2013


Limite de la propriété

Morcellement de T.239/25 (P.1) (Lot 16)

S.F.80

NORD الشمال

Plan produit par le requérant
Scan vérifié à la date:.....
Fusion Totale faite par : SYNERGIE TOPO
Du : Janvier 2024

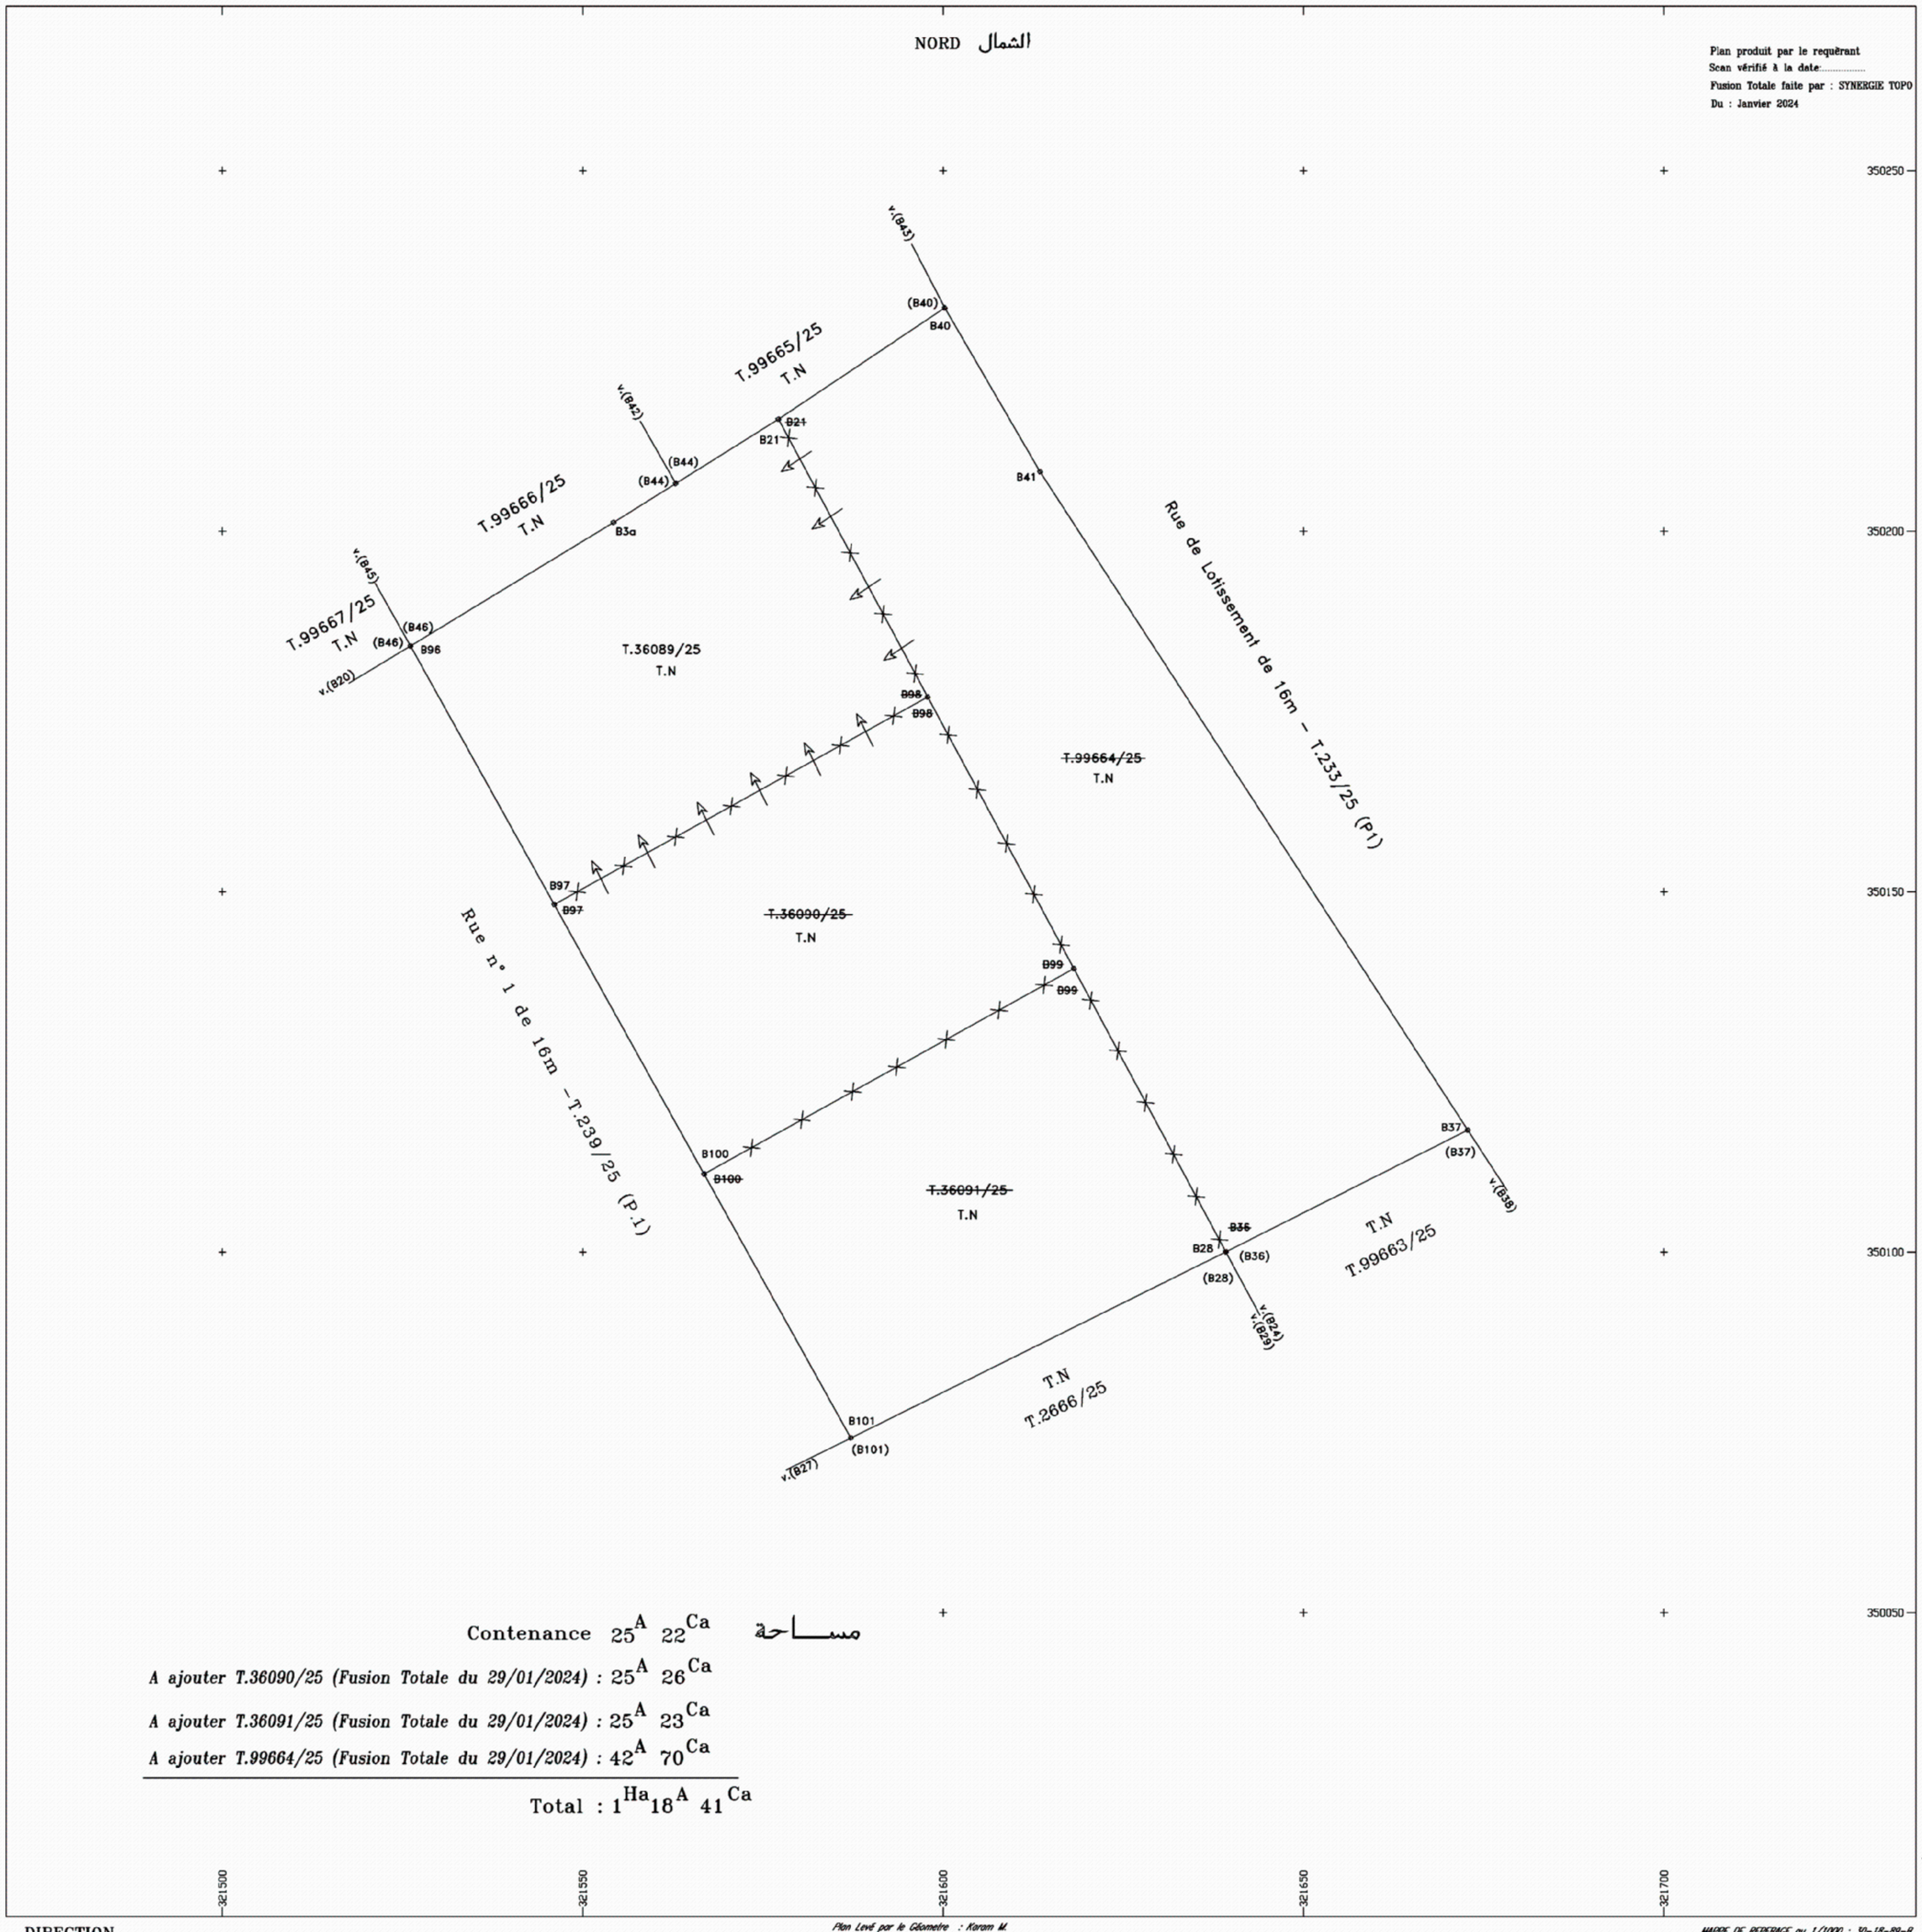

Contenance $25^{A}\ 22^{Ca}$ مساحة

A ajouter T.36090/25 (Fusion Totale du 29/01/2024) : $25^{A}\ 26^{Ca}$

A ajouter T.36091/25 (Fusion Totale du 29/01/2024) : $25^{A}\ 23^{Ca}$

A ajouter T.99664/25 (Fusion Totale du 29/01/2024) : $42^{A}\ 70^{Ca}$

Total : $1^{Ha}18^{A}\ 41^{Ca}$

الملك المسمى : جوهرة البحر 16

المكان : اقليم بن سليمان جماعة المنصورية تجزئة جوهرة البحر

رسم : 25/36089

تجزئة الرسم : 26/239 (قسيمة 1) — (بقعة : 16)

DIRECTION DU CADASTRE

Plan Levé par le Géometre : Karam M.
Dessiné par : Naima A.
CT EL YOUSFI DRISS OULAHCEN

MAPPE DE REPERAGE au 1/1000 : 30-18-89-8
Carte Topographique au 1/20 000 Benslimane

Digitally signed by ADDI SOUAD
Date: 2025.08.05 15:32:38 +01:00
Code de vérification en ligne : 250118a5-68b0-4e8a-ab2f-65e01dcfc8d8